
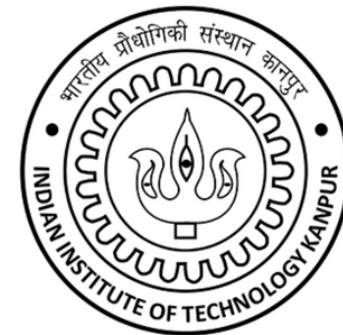
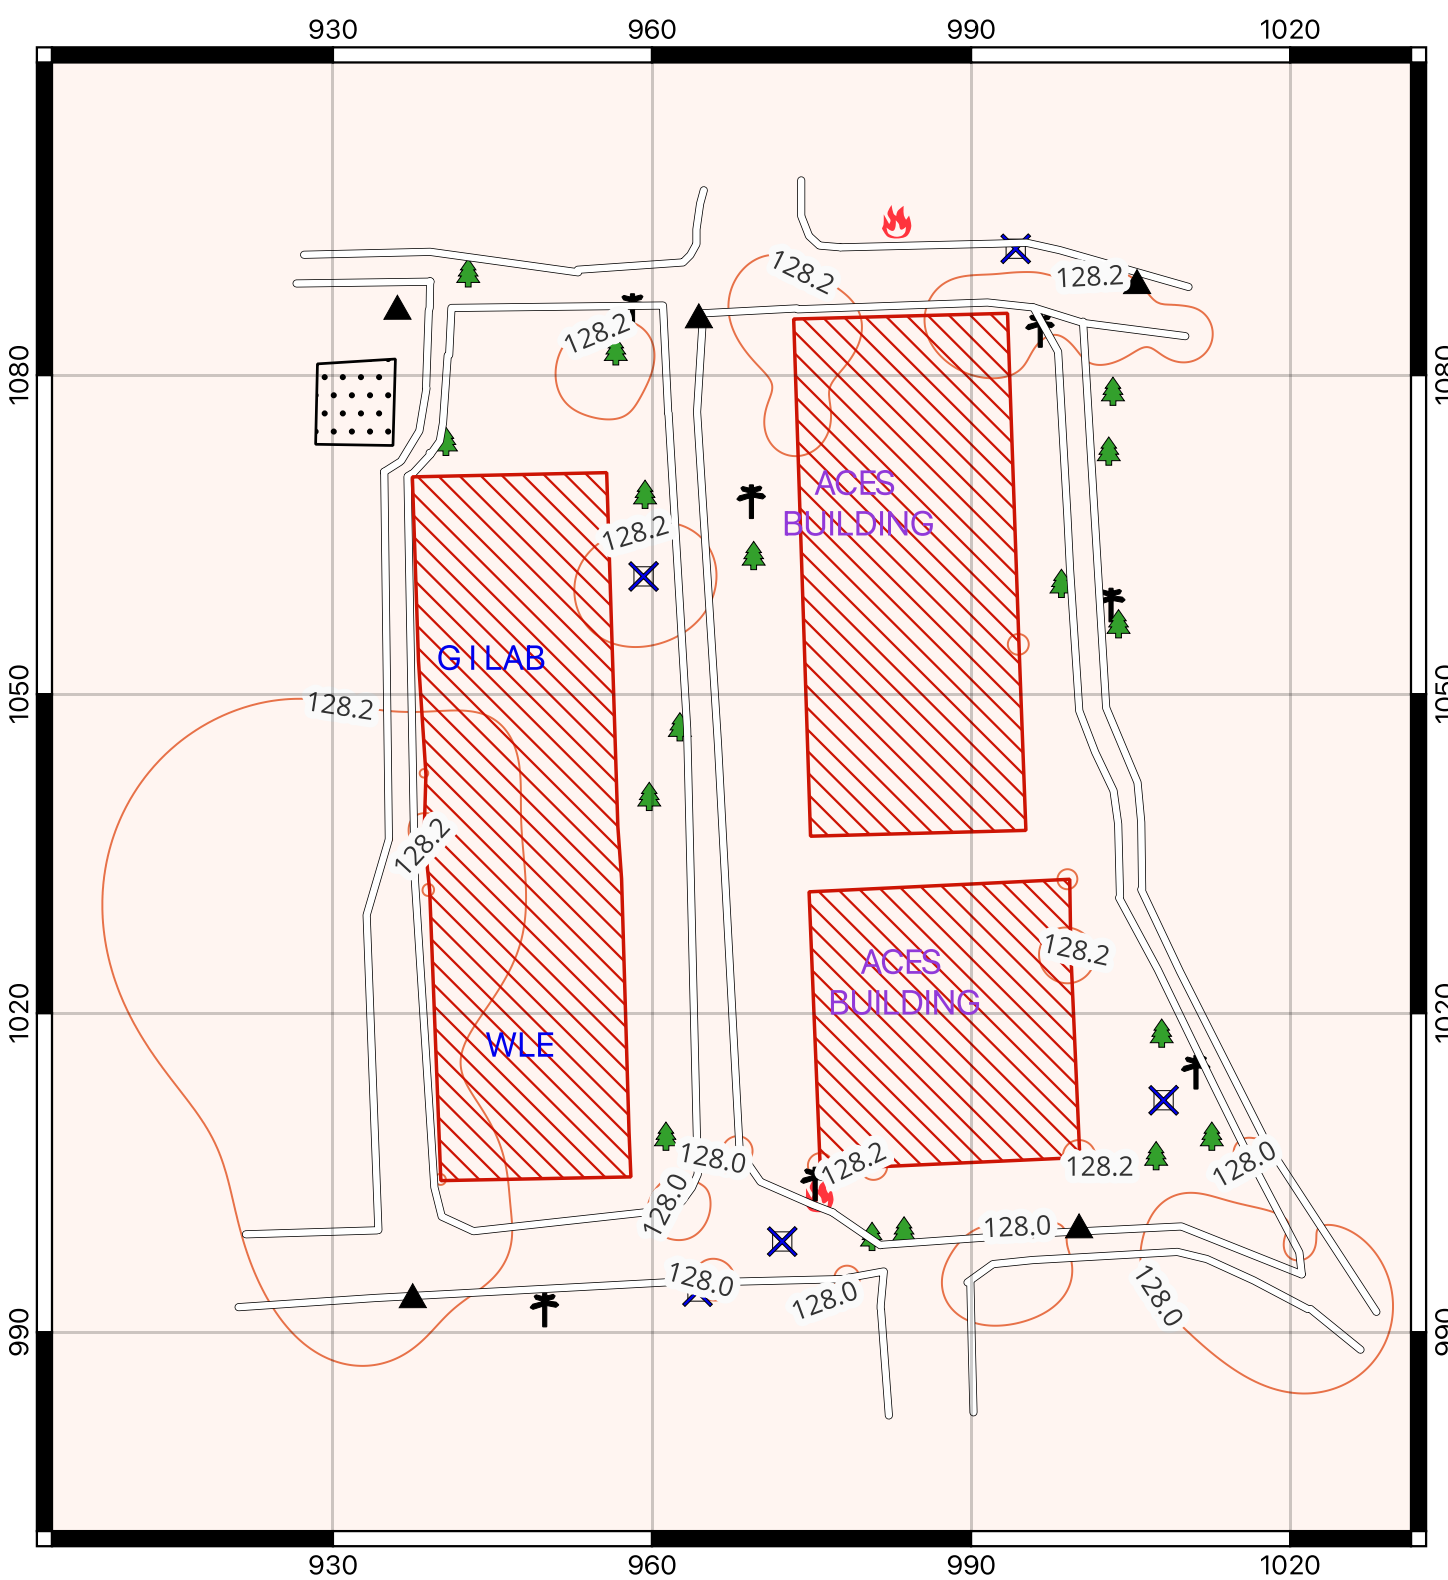


SCALE 1 : 750

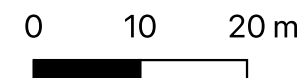

GI LAB & ACES BUILDING

Contour Interval : 0.2 m

Instructor : Prof. Salil Goel

TA: Jamil Mahmood

GROUP 7 TUESDAY

Group members:

Anurag Sharma(230174)

Awnish Kumar(230250)

Himanshu Dugar(230472)

Siddharth Jaiswal(231005)

Subhankar Sutradhar(231042)

MAP LEGEND

Building	ELECTRIC POLE
WATER TANK	MANHOLE
CP	FIRE HYDRANT
ROADS	contours
TREE	